
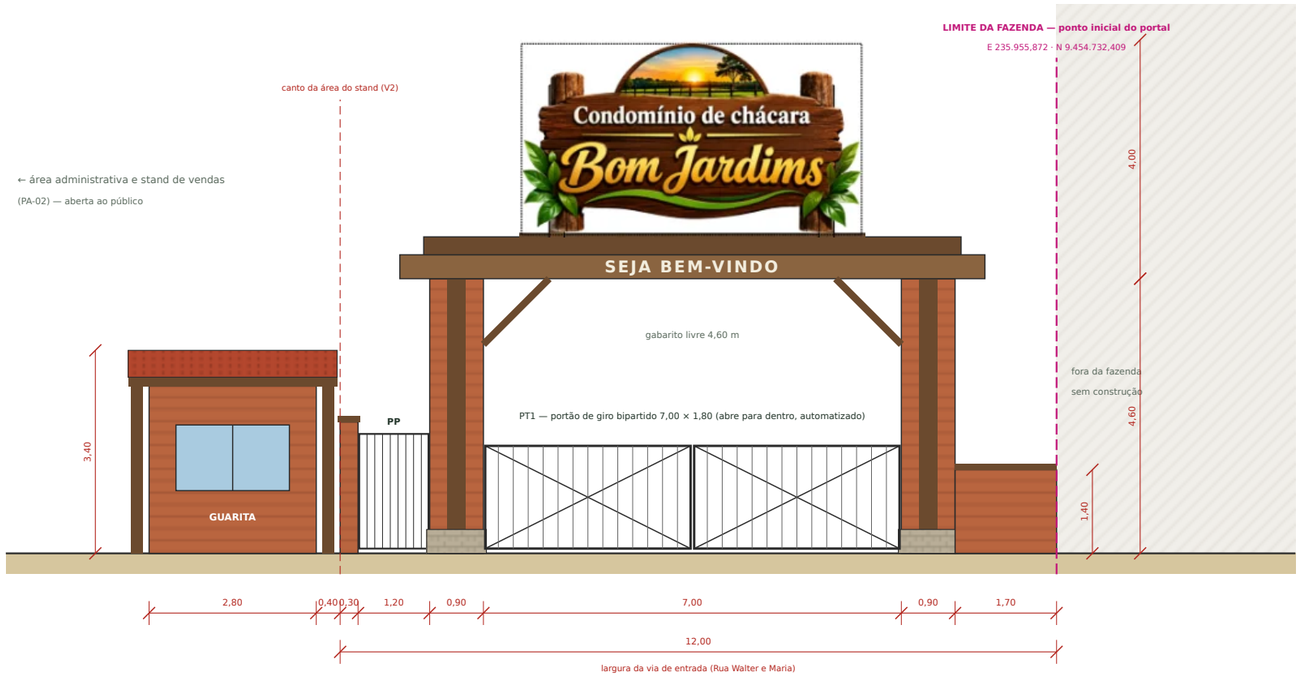


FACHADA FRONTAL escala 1:100

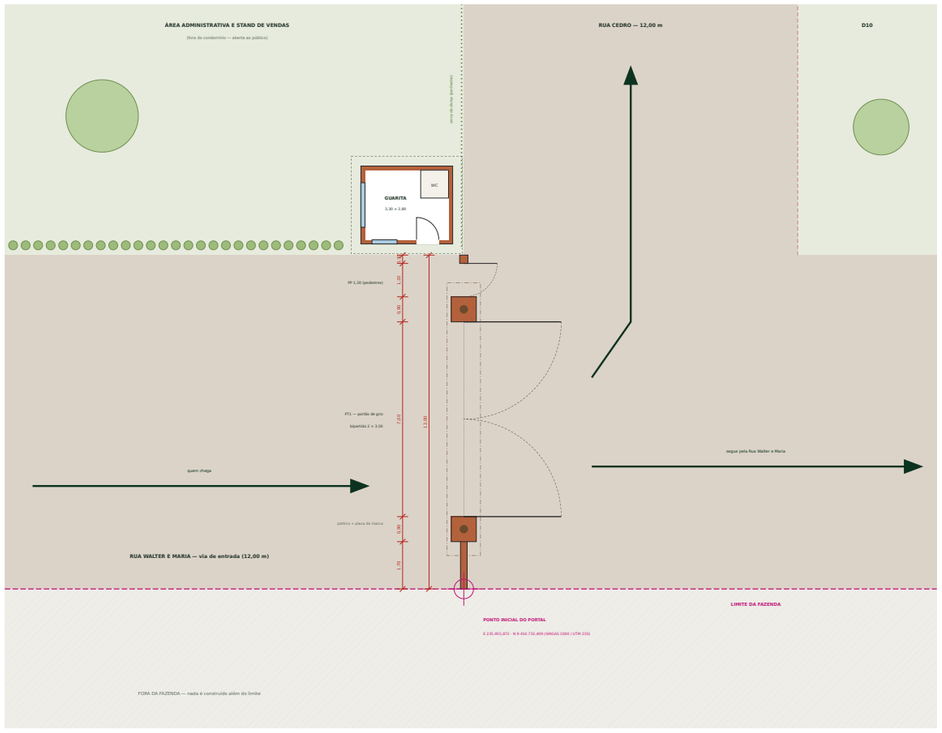

PLANTA BAIXA escala 1:100 (reduzida para caber na folha)

NOTAS

1. Portal atravessando a via de entrada (Rua Walter e Maria, 12,00 m), na esquina com a Rua Cedro. Ponto inicial no limite da fazenda: E 235.955,872 · N 9.454.732,409 (SIRGAS 2000 / UTM 23S).
2. Nenhum elemento além do ponto inicial: todo o conjunto é projetado da linha do limite da fazenda para dentro, até o canto da área administrativa / stand.
3. Sem ala lateral: de um lado o limite da fazenda (mureta de arremate até o ponto inicial), do outro a área do stand, aberta ao público.
4. Guarita 2,80 × 3,30 m na área administrativa, junto ao portão de pedestres, com WC, porta para a via e janelas para o portão e para o stand.
5. Portão principal PT1 de giro, bipartido (2 × 3,50 × 1,80 m), abrindo para dentro, com automatizador. Depois do portal o fluxo segue pela Rua Cedro ou pela Rua Walter e Maria.
6. Pórtico em toras com revestimento em tábuas e base em pedra; gabarito livre de 4,60 m; placa da marca e "SEJA BEM-VINDO" na viga.
7. Divisa da área administrativa com a Rua Cedro: cerca de divisa (alambrado com cerca viva) para que o acesso ao condomínio seja só pelo portal.
8. Medidas em metros. NBR 6492 (representação de projetos de arquitetura) e NBR 9050 (portão de pedestres com vão livre ≥ 0,80 m).


FACHADA E PLANTA BAIXA

Portal de entrada — PA-01 rev. V2

Condomínio de Chácaras Bom Jardims — Açailândia/MA
Via de entrada: Rua Walter e Maria, esquina com a Rua Cedro

Responsável técnico: José Romário
Técnico em Edificações · Técnico em Agrimensura — CFT/MA 01209185369
INCRA FQNS · Corretor CRECI/MA F-4.705
Romatec Consultoria Total · (99) 9 9181-1246
Folha 1/2 · A3 · 09/11/2026 · substitui PA-01 (portal com alas laterais)

Assinatura do responsável técnico

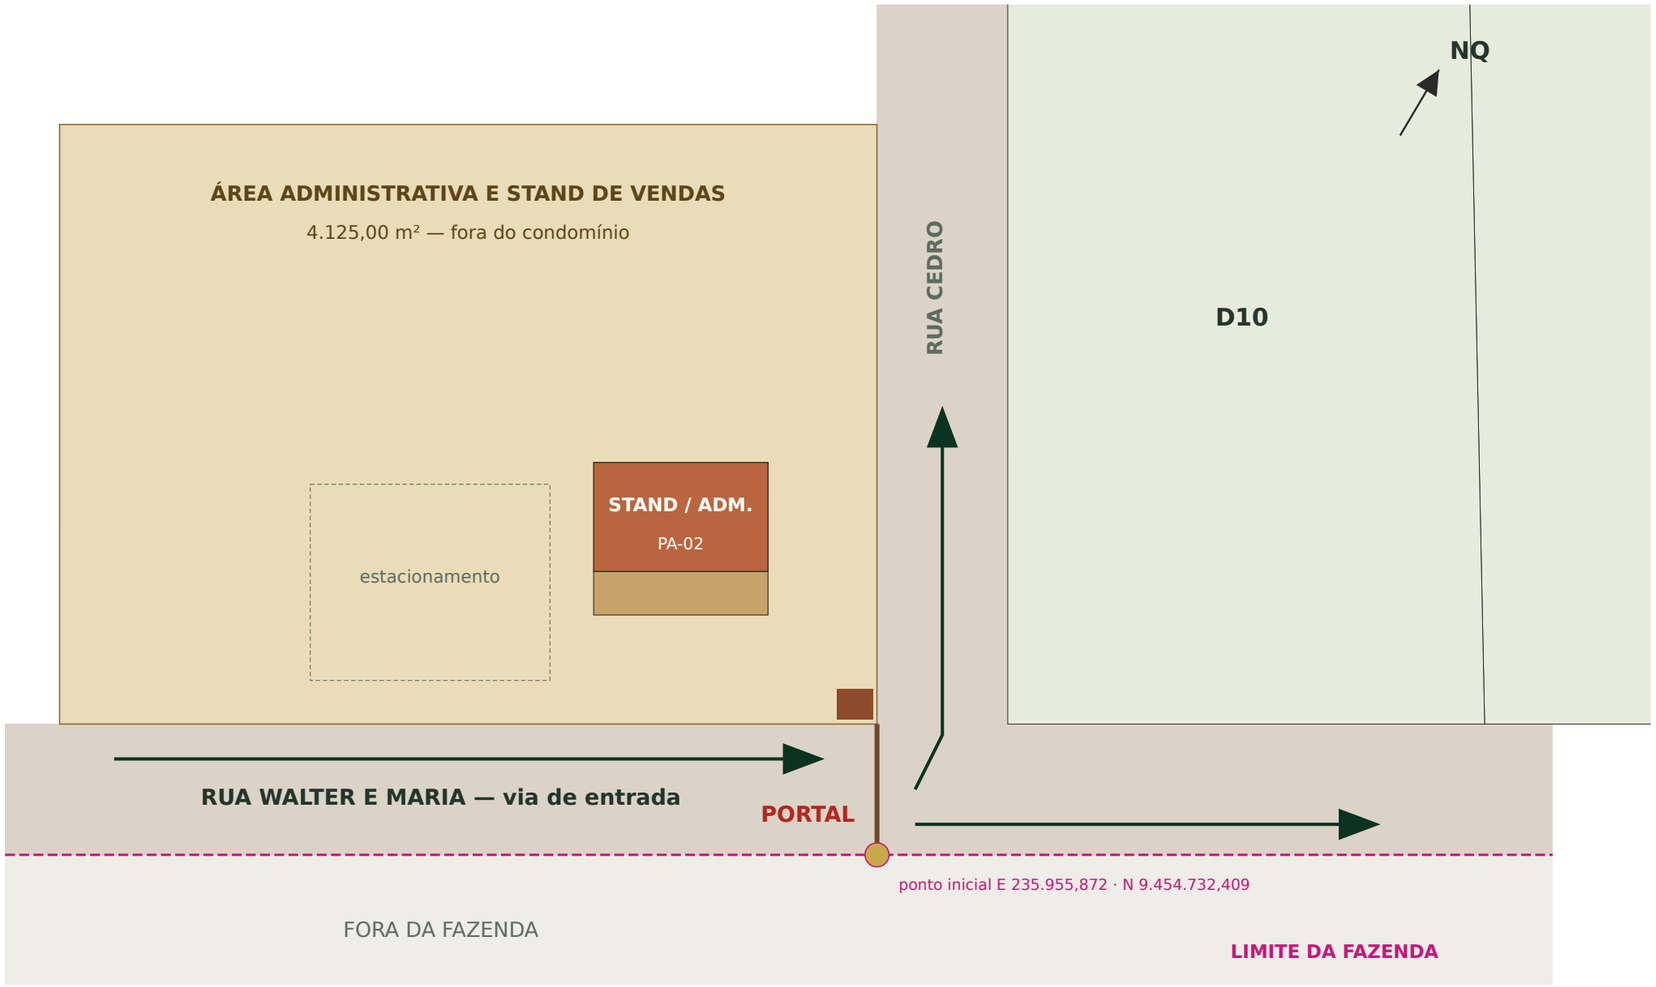

IMPLANTAÇÃO GERAL escala 1:500

NOTAS

1. Geometria do terreno da área administrativa e dos lotes: DXF "Condomínio de Chácaras Bom Jardims — atualizado V2" (SIRGAS 2000 / UTM 23S).
2. Área administrativa e stand de vendas: 4.125,00 m² (75,00 × 55,00 m), fora do perímetro do condomínio.
3. Edificação PA-02 (16,00 × 10,00 m + varanda 16,00 × 4,00 m) e estacionamento: implantação proposta, sujeita a aprovação municipal.
4. Confrontações da área administrativa a conferir em campo pelo responsável técnico (NBR 13133).
5. Escala 1:500 (A3).

IMPLANTAÇÃO

Portal de entrada — PA-01 rev. V2

Condomínio de Chácaras Bom Jardims — Açailândia/MA

Via de entrada: Rua Walter e Maria, esquina com a Rua Cedro

Responsável técnico: José Romário
Técnico em Edificações · Técnico em Agrimensura — CFT/MA 01209185369
INCRA FQNS · Corretor CRECI/MA F-4.705
Romatec Consultoria Total · (99) 9 9181-1246

Folha 2/2 · A3 · 09/11/2026 · substitui PA-01 (portal com alas laterais)

Assinatura do responsável técnico