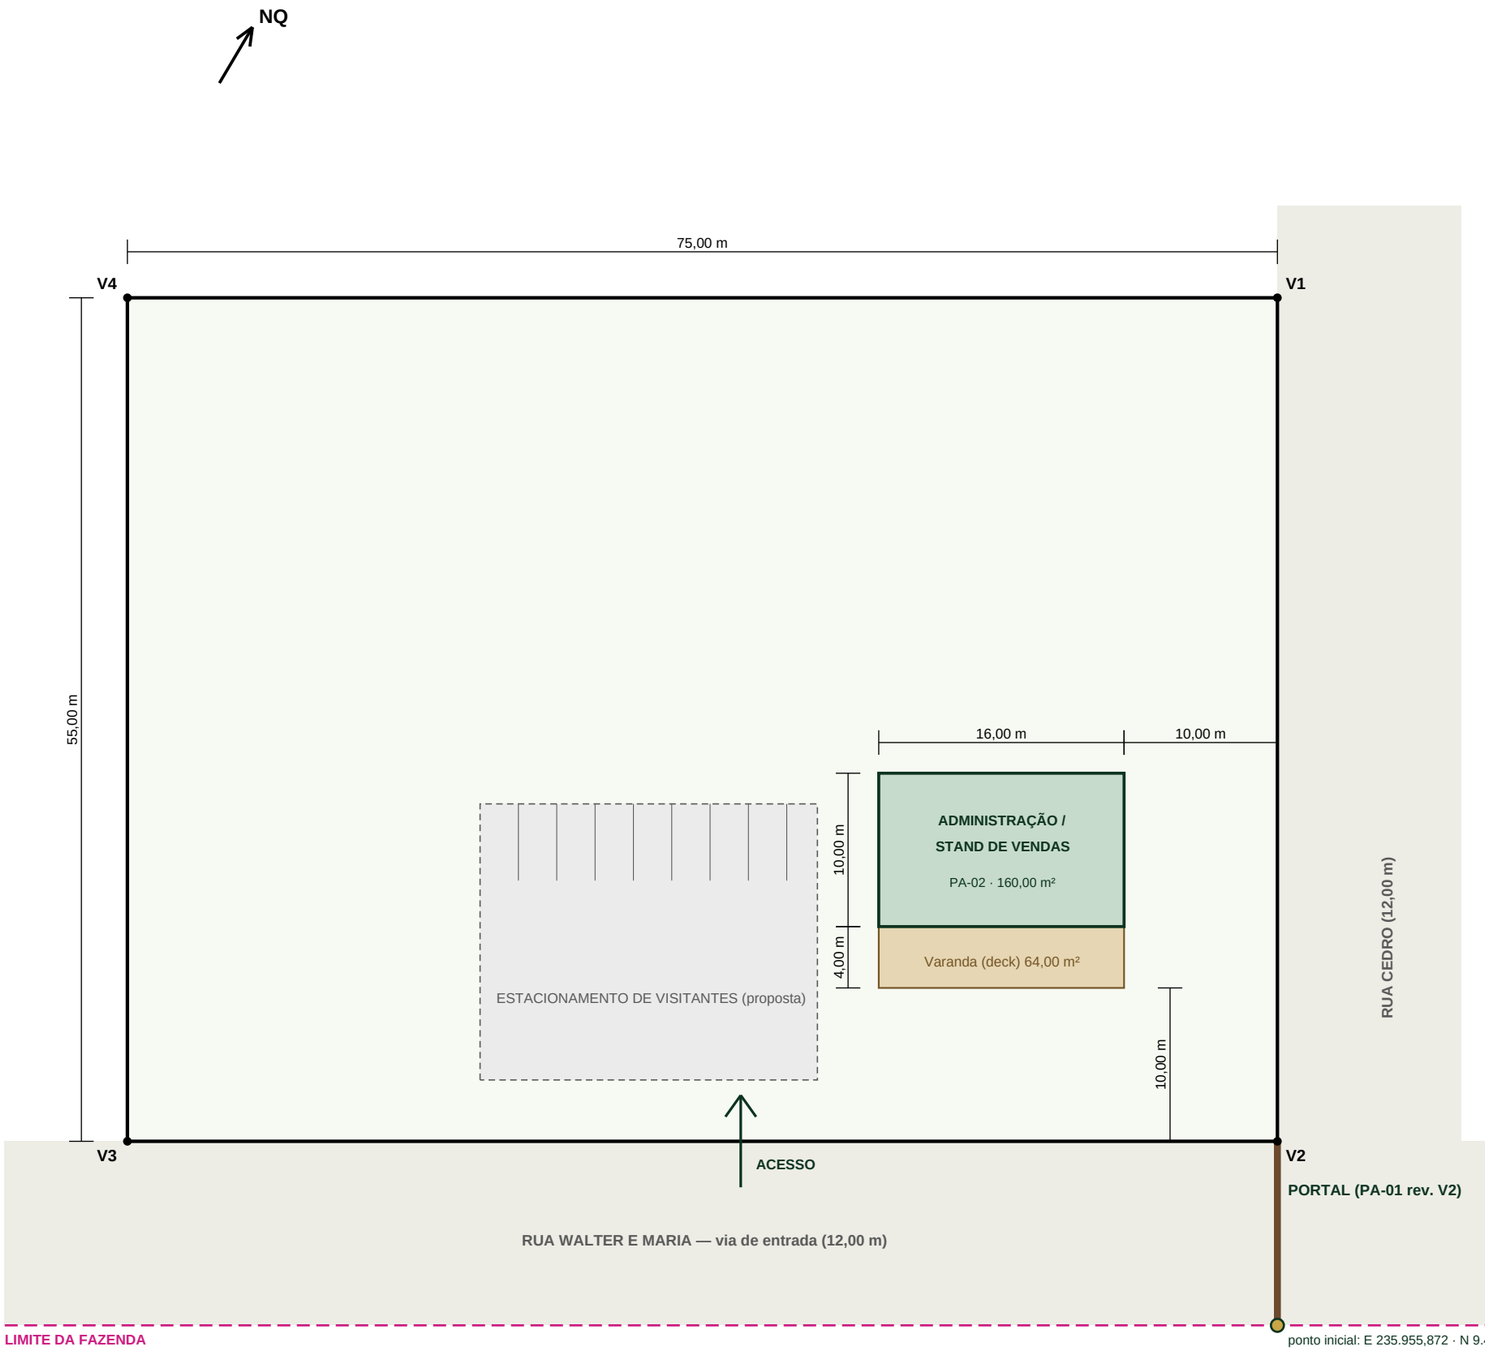

IMPLANTAÇÃO — ÁREA ADMINISTRATIVA E STAND DE VENDAS

Escala 1:400

QUADRO DE VÉRTICES — SIRGAS 2000 / UTM 23S

Vért.	E (m)	N (m)	Azimute	Dist. (m)	Confrontação
V1	235.921,722	9.454.790,053	149°21'20"	55,00	Rua Cedro
V2	235.949,756	9.454.742,734	239°21'22"	75,00	Rua Walter e Maria
V3	235.885,229	9.454.704,506	329°21'23"	55,00	Remanescente*
V4	235.857,196	9.454.751,825	59°21'20"	75,00	Remanescente*

* Confrontações a conferir em campo pelo responsável técnico.

QUADRO DE ÁREAS

Área do terreno (administrativa e vendas)	**4.125,00 m²**
Perímetro	**260,00 m**
Área construída (PA-02)	**160,00 m²**
Varanda em deck de madeira	**64,00 m²**
Taxa de ocupação	**5,43 %**
Área livre / permeável	**3.901,00 m²**

NOTAS

Área administrativa e stand de vendas fora do perímetro do condomínio, na entrada, junto ao portal (Rua Walter e Maria × Rua Cedro), projeto V2.

Geometria do terreno do levantamento do parcelamento (DXF "Condomínio de Chácaras Bom Jardims — atualizado V2").

Edificação: projeto arquitetônico PA-02 (16,00 × 10,00 m) com varanda de 16,00 × 4,00 m voltada para a Rua Walter e Maria.

Posição da edificação e do estacionamento: proposta de implantação, sujeita a aprovação municipal.

Coordenadas planas UTM, SIRGAS 2000, fuso 23 Sul. Azimutes e distâncias planos. NBR 13133 e NBR 6492.

Medidas em metros. Escala 1:400 (A3).

PLANTA DE IMPLANTAÇÃO

Área administrativa e stand de vendas

Condomínio de Chácaras Bom Jardims — Açailândia/MA

Estrada do Piquiá dos Baianos, altura do km 15 da BR-222

Responsável técnico: José Romário
Técnico em Agrimensura — CFT/MA 01209185369 · INCRA FQNS
Técnico em Edificações · Corretor CRECI/MA F-4.705
Romatec Consultoria Total · CRECI J-1234 · (99) 9 9181-1246

Escala 1:400 · Folha A3 · Data: 09/11/2026 · Projeto V2

Assinatura do responsável técnico